

PROJECT

RESTAURANT KITCHEN FIT-OUT
Ground Floor — Kitchen, Stores & Dining

CLIENT

DRAWING TITLE

GROUND FLOOR LAYOUT
Kitchen Equipment Plan & Schedule

LEGEND

- 01 Cold prep equipment tag (see schedule)
- 01 Hot prep equipment tag (see schedule)
- Cold room insulated panel wall
- Cooking equipment / ovens
- Refrigeration units, doors & glazing
- Sinks & wash area fixtures
- Structural column
- Loose furniture (dining & bar)
- Dimension line (mm)

GENERAL NOTES

- All dimensions are in millimetres unless otherwise stated.
- Do not scale from this drawing. All dimensions to be verified on site before fabrication.
- S/S = stainless steel. Cabinet height shown as 850+100 = worktop height + upstand/leg allowance per schedule.
- FFL = finished floor level. Dry store & wash area at FFL +0.1 m.
- Dining tables 800 x 800 mm typical.
- Cold prep and hot prep items are numbered separately; refer to the tag colour.
- Existing refrigeration units to be retained in the positions shown.

CLIENT APPROVAL

Signature / Stamp / Date

REVISIONS


REV	DATE	DESCRIPTION
R0	28.09.2026	First issue for review

DRAWN BY S. ANTONY	CHECKED BY
DATE 28.09.2026	SCALE 1:80 @ A3
SHEET 01 OF 01	REVISION R0

DRAWING NO.

TNDK-GF-A-01

R0

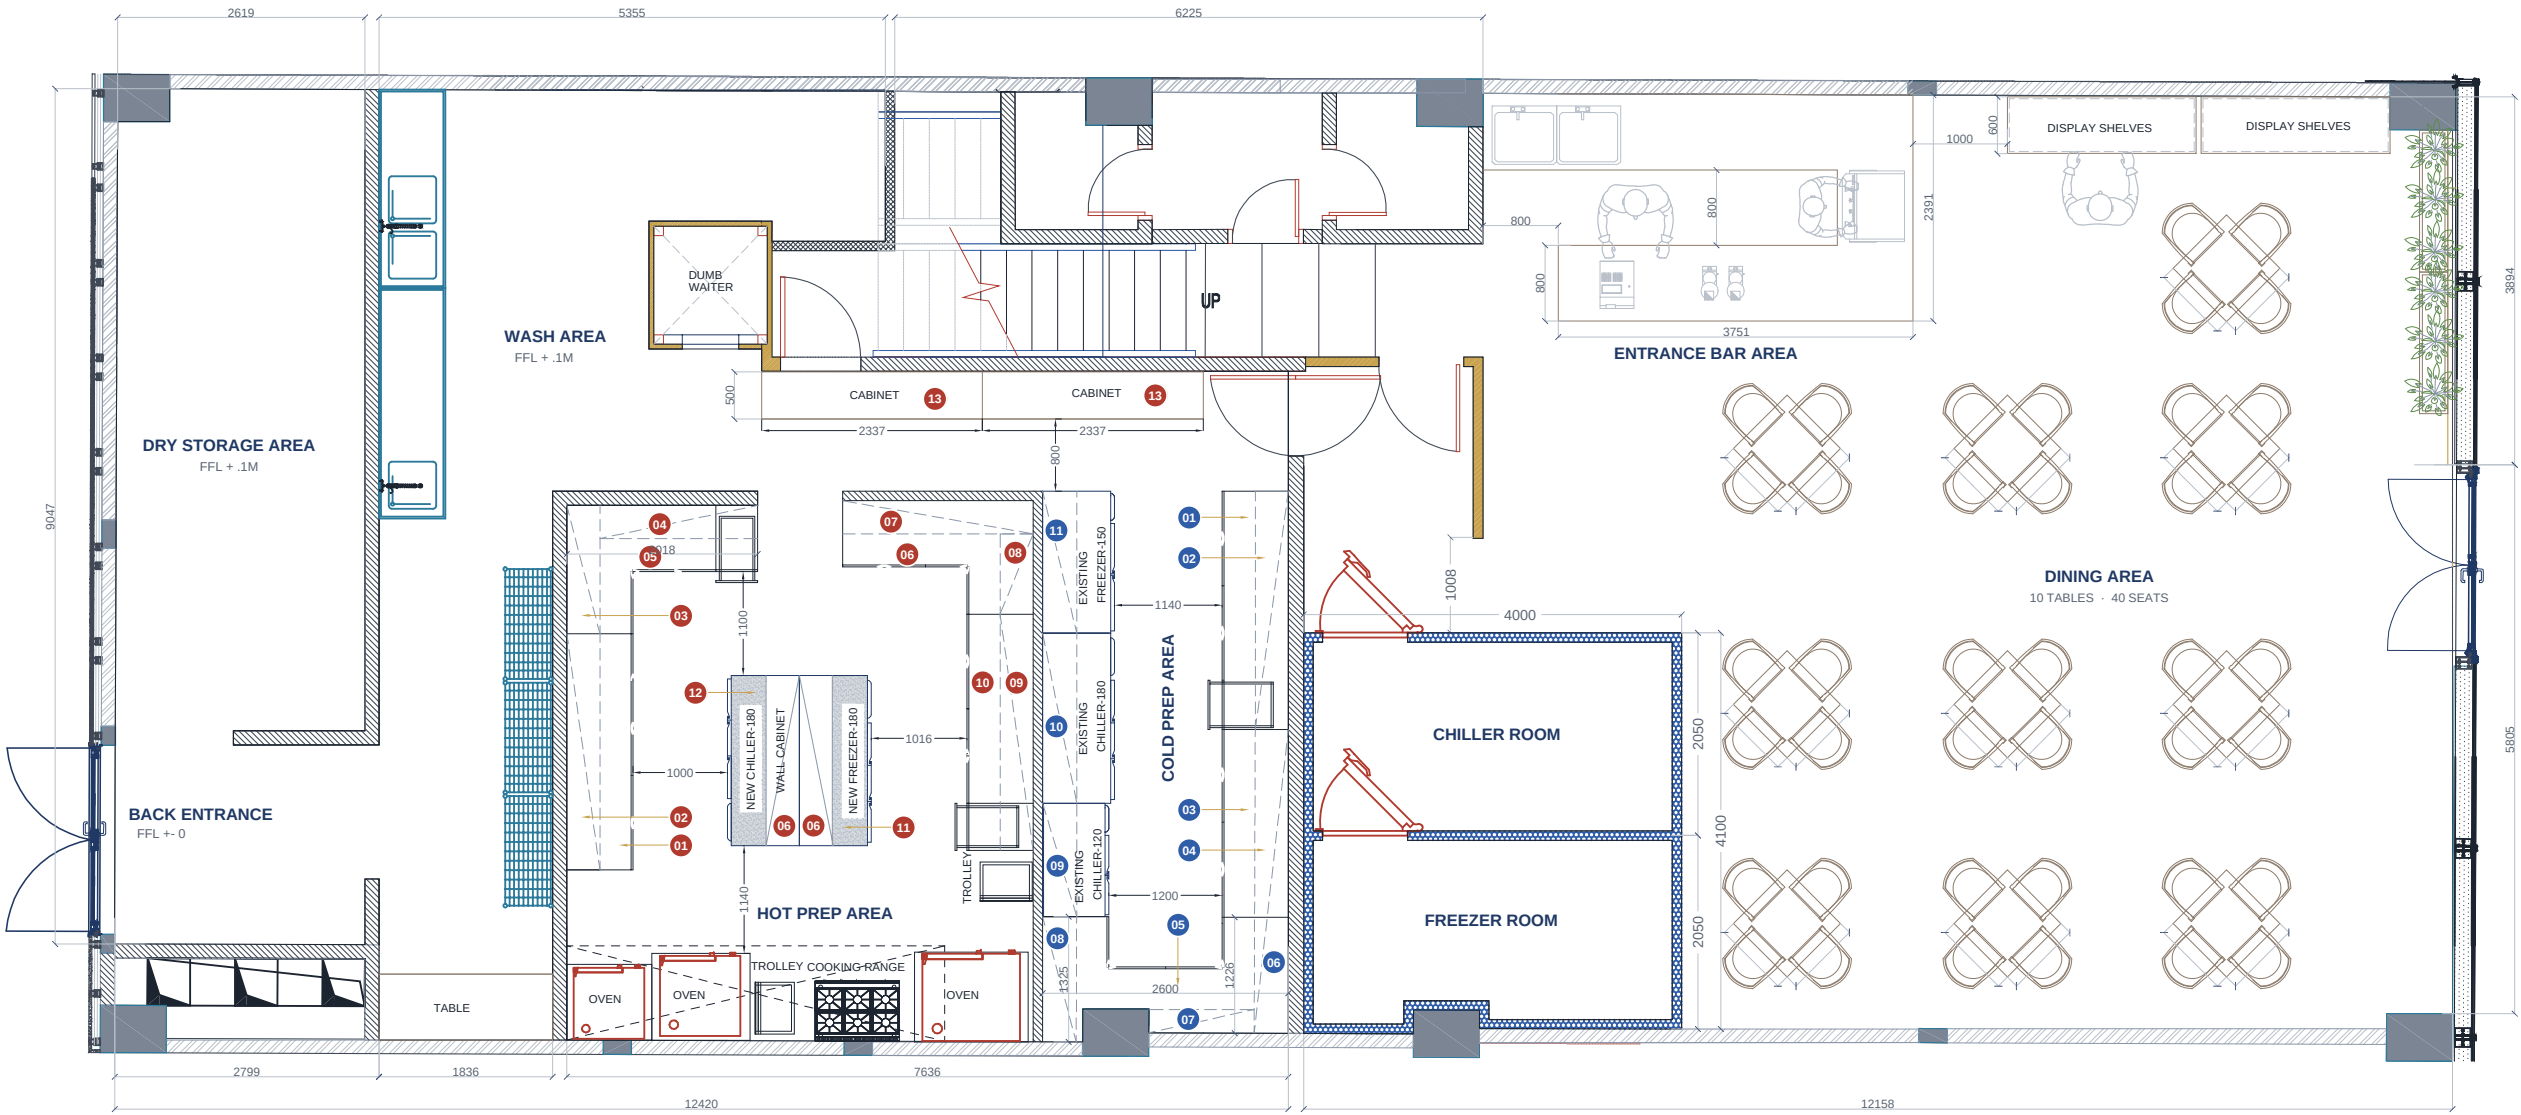

01 GROUND FLOOR LAYOUT
A-01 KITCHEN EQUIPMENT & DINING ARRANGEMENT | SCALE 1:80 @ A3



EQUIPMENT SCHEDULE — COLD PREP AREA				11 LINE ITEMS
TAG	DESCRIPTION	SIZE L x W x H (mm)	QTY	
01	S/S BASE CABINET WITH MIDDLE & UNDER SHELF, HINGED DOOR, BACK SPLASH + 3 NOS DRAWERS	2500 x 700 x 850+100	01	
02	S/S TWO LEVEL OVER SHELF	2500 x 350 x 800	01	
03	S/S BASE CABINET WITH MIDDLE & UNDER SHELF, HINGED DOOR, BACK SPLASH	1987 x 700 x 850+100	01	
04	S/S TWO LEVEL OVER SHELF	1987 x 350 x 800	01	
05	S/S C-SHAPE BASE CABINET WITH MIDDLE & UNDER SHELF, BACK SPLASH	1325+2600+1226 x 700 x 850+100	01	
06	S/S TWO LEVEL OVER SHELF	1225 x 350 x 800	01	
07	S/S TWO LEVEL OVER SHELF	2600 x 350 x 800	01	
08	S/S TWO LEVEL OVER SHELF	1325 x 350 x 800	01	
09	S/S TWO LEVEL OVER SHELF	1200 x 350 x 800	01	
10	S/S TWO LEVEL OVER SHELF	1800 x 350 x 800	01	
11	S/S TWO LEVEL OVER SHELF	1500 x 350 x 800	01	
TOTAL UNITS			11	

EQUIPMENT SCHEDULE — HOT PREP AREA				13 LINE ITEMS
TAG	DESCRIPTION	SIZE L x W x H (mm)	QTY	
01	S/S BASE CABINET WITH MIDDLE & UNDER SHELF, HINGED DOOR, BACK SPLASH + 3 NOS DRAWERS	2500 x 700 x 850+100	01	
02	S/S TWO LEVEL OVER SHELF	2500 x 350 x 800	01	
03	S/S TWO LEVEL OVER SHELF	1357 x 350 x 800	01	
04	S/S TWO LEVEL OVER SHELF	1668 x 350 x 800	01	
05	S/S CORNER BASE CABINET WITH MIDDLE & UNDER SHELF, HINGED DOORS + 3 NOS DRAWERS	1357+2018 x 700 x 850+100	01	
06	S/S TWO LEVEL OVER SHELF	1800 x 350 x 800	02	
07	S/S TWO LEVEL OVER SHELF	2018+1200 x 700 x 850+100	01	
08	S/S TWO LEVEL OVER SHELF	850 x 350 x 800	01	
09	S/S TWO LEVEL OVER SHELF	2500 x 350 x 800	01	
10	S/S BASE CABINET WITH MIDDLE & UNDER SHELF, HINGED DOOR, BACK SPLASH + 3 NOS DRAWERS	2500 x 700 x 850+100	01	
11	WORK TOP FREEZER - 180	1800 x 760 x 840	01	
12	WORK TOP CHILLER - 180	1800 x 760 x 840	01	
13	S/S BASE CABINET WITH MIDDLE & UNDER SHELF, HINGED DOOR, BACK SPLASH	2337 x 500 x 850+100	02	
TOTAL UNITS			15	