

THE NEW DOHA KITCHEN
EQUIPMENT SERVICES W.L.L.

Commercial Kitchen & Cold Storage Solutions
P.O. Box 80247, Doha, Qatar | info@dgeqatar.com

PROJECT

RESTAURANT KITCHEN FIT-OUT

Ground Floor — Kitchen, Stores & Dining

DRAWING TITLE

PROPOSED LAYOUT

Kitchen Equipment Rearrangement — Option A

FOR CLIENT REVIEW — NOT FOR FABRICATION

LEGEND

- 01 Cold prep item tag
- 01 Hot kitchen item tag
- N1 New item recommended by consultant
- S/S fabrication (base cabinet / table)
- Over shelf above counter
- New refrigeration (work top units)
- Existing refrigeration — retained
- Cooking equipment (existing, re-sequenced)
- New sink / hand wash basin
- Goods-in route
- Food service route
- Dirty return route

KEY CHANGES

- Centre island removed. W/T chiller & freezer now form a chef base opposite the range with a 1200 mm cook aisle.
- Peninsula carries a pass shelf (06) so plated food leaves via the north aisle without crossing the cook line.
- Range moved 850 mm left, trolley out of the line, 900 mm landing table (10) added.
- Prep zone separated from cooking: 1380 mm prep aisle, 1390 mm clear route from door to cook line.
- Corridor cabinets (13) moved to dry store: corridor widens 800 → 1290 mm.
- Prep sink N1 and hand wash basins N2 / N3 added (MEP to confirm).

CLEARANCE CHECK (mm)

Location	Existing	Proposed
Cook aisle	1140	1200
Door to cook line	1000	1390
Hot prep aisle	1016	1380
Corridor	800	1290


REVISIONS

R0	28.09.2026	Existing layout (A-01)
P1	29.09.2026	Proposed rearrangement
PREPARED BY TNDK DESIGN	CHECKED BY	
DATE 29.09.2026	SCALE 1:80 @ A3	
SHEET 01 OF 02	REVISION P1	

DRAWING NO.

TNDK-GF-A-02

P1

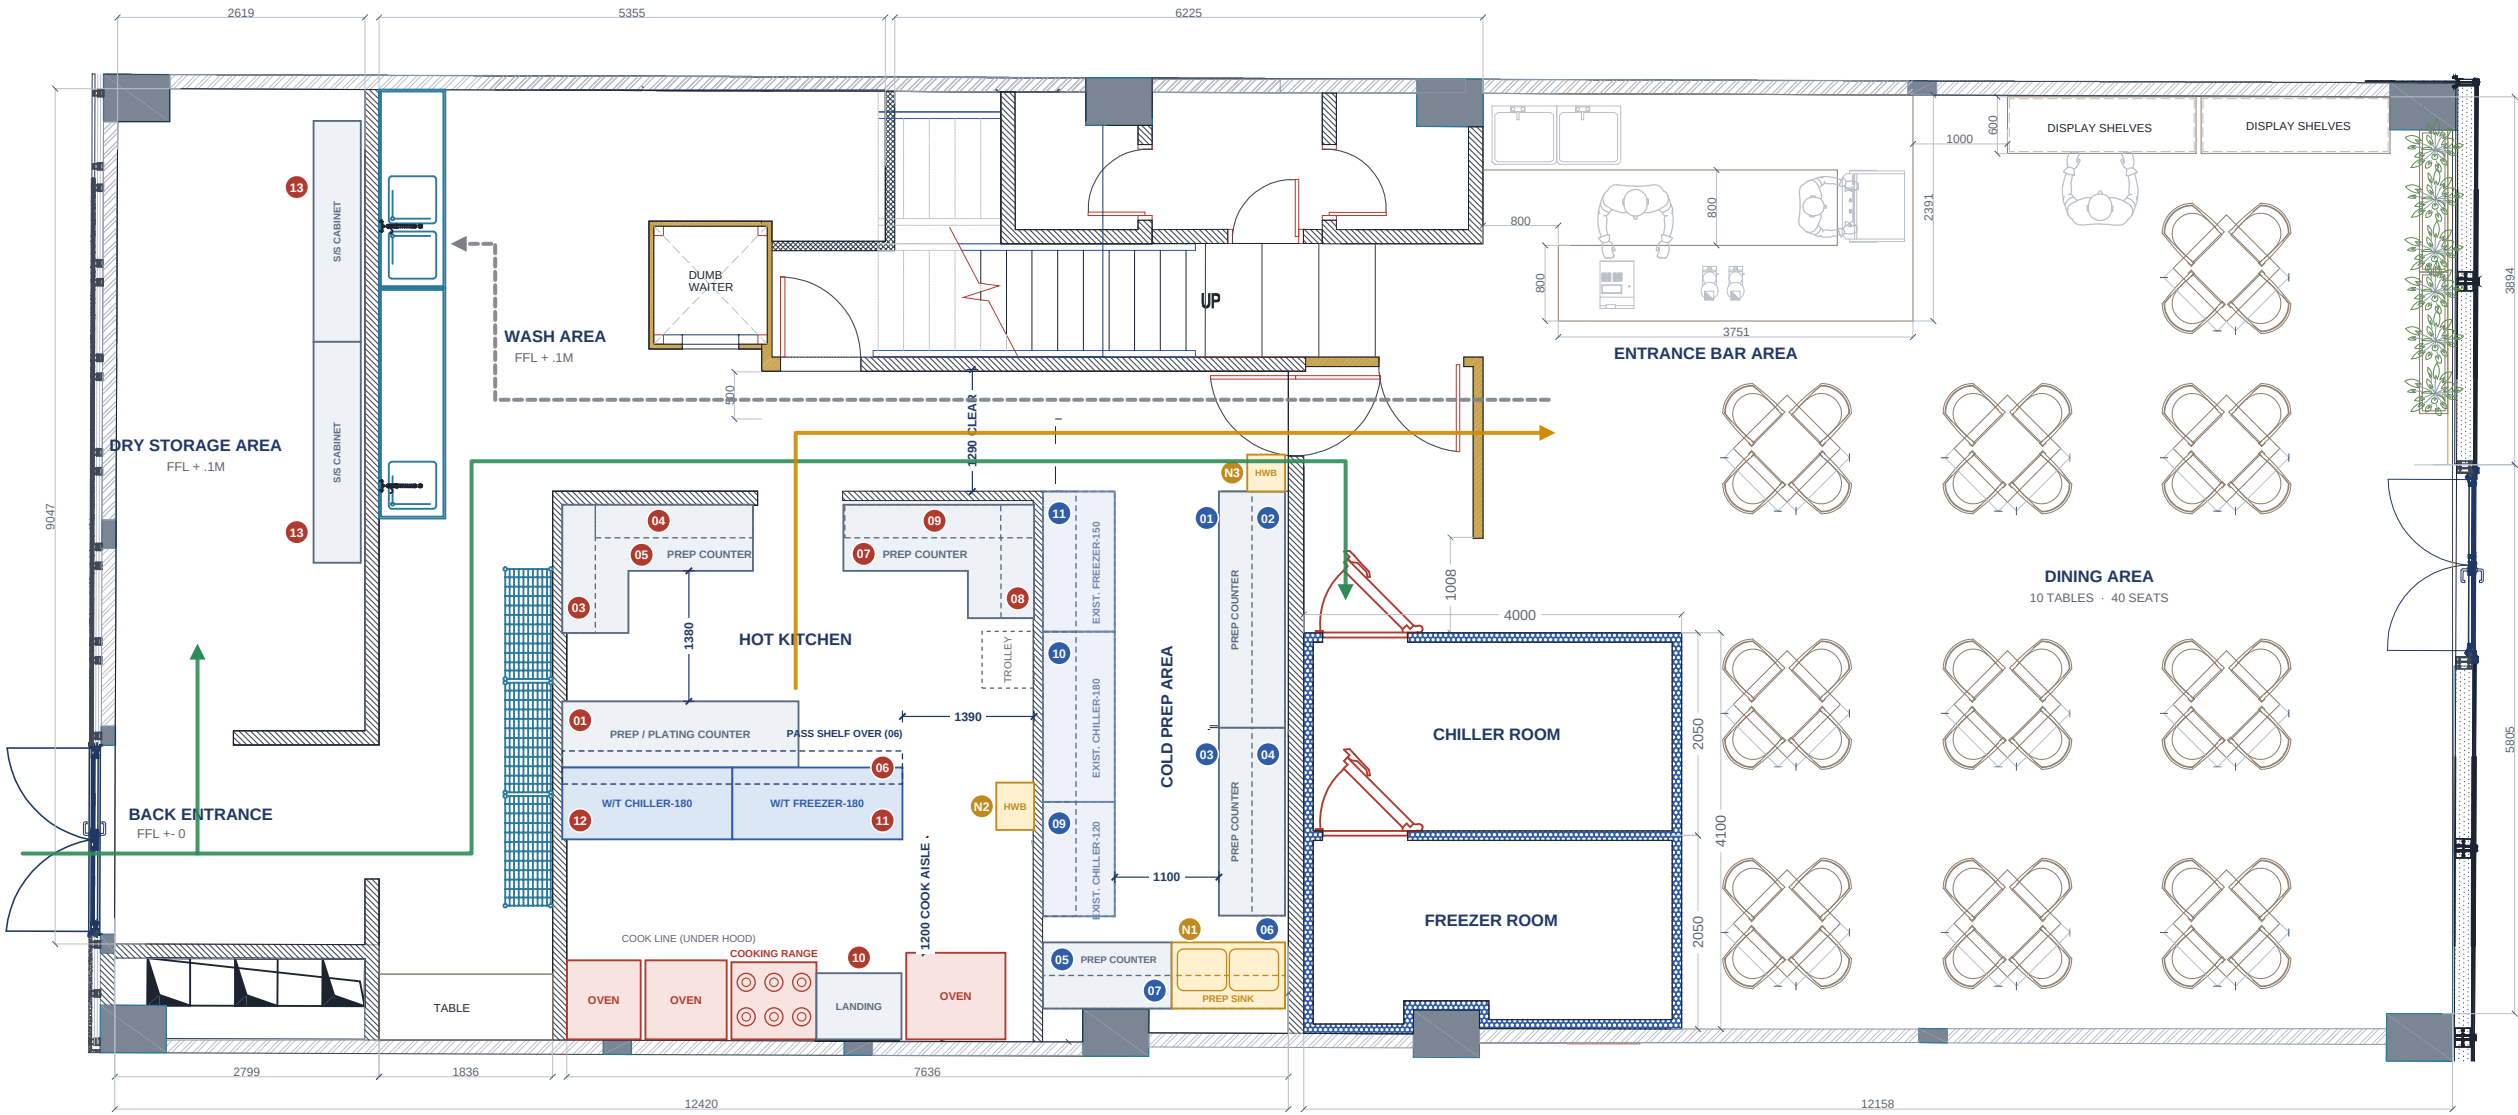

01
A-02

PROPOSED GROUND FLOOR LAYOUT

KITCHEN EQUIPMENT REARRANGEMENT — CONSULTANT OPTION A | SCALE 1:80 @ A3

GOODS IN

FOOD SERVICE

DIRTY RETURN

GRAPHIC SCALE



PROPOSED SCHEDULE — COLD PREP AREA

11 ITEMS + 2 NEW

TAG	DESCRIPTION	SIZE L x W x H (mm)	QTY	STATUS
01	S/S BASE CABINET, MIDDLE & UNDER SHELF, HINGED DOOR, BACK SPLASH + 3 DRAWERS	2500 x 700 x 850+100	01	RETAINED
02	S/S TWO LEVEL OVER SHELF	2500 x 350 x 800	01	RETAINED
03	S/S BASE CABINET, MIDDLE & UNDER SHELF, HINGED DOOR, BACK SPLASH	1987 x 700 x 850+100	01	RETAINED
04	S/S TWO LEVEL OVER SHELF	1987 x 350 x 800	01	RETAINED
05	S/S BASE CABINET, MIDDLE & UNDER SHELF, BACK SPLASH (WAS C-SHAPE)	1360 x 700 x 850+100	01	RESIZED
06	S/S TWO LEVEL OVER SHELF — MOVED ABOVE PREP SINK N1	1225 x 350 x 800	01	RELOCATED
07	S/S TWO LEVEL OVER SHELF	1360 x 350 x 800	01	RESIZED
08	S/S TWO LEVEL OVER SHELF — NO LONGER REQUIRED	1325 x 350 x 800	01	OMIT
09	S/S TWO LEVEL OVER SHELF (ABOVE EXIST. CHILLER-120)	1200 x 350 x 800	01	RETAINED
10	S/S TWO LEVEL OVER SHELF (ABOVE EXIST. CHILLER-180)	1800 x 350 x 800	01	RETAINED
11	S/S TWO LEVEL OVER SHELF (ABOVE EXIST. FREEZER-150)	1500 x 350 x 800	01	RETAINED
N1	S/S DOUBLE BOWL PREP SINK WITH BACK SPLASH & UNDER SHELF	1200 x 700 x 850+100	01	NEW
N3	S/S HAND WASH BASIN, KNEE / SENSOR OPERATED	400 x 400	01	NEW

PROPOSED SCHEDULE — HOT KITCHEN


13 ITEMS + 1 NEW

TAG	DESCRIPTION	SIZE L x W x H (mm)	QTY	STATUS
01	S/S BASE CABINET + 3 DRAWERS — PENINSULA PREP / PLATING FACE	2500 x 700 x 850+100	01	RELOCATED
02	S/S TWO LEVEL OVER SHELF — REPLACED BY PASS SHELF 06	2500 x 350 x 800	01	OMIT
03	S/S TWO LEVEL OVER SHELF	1357 x 350 x 800	01	RETAINED
04	S/S TWO LEVEL OVER SHELF	1668 x 350 x 800	01	RETAINED
05	S/S CORNER BASE CABINET, HINGED DOORS + 3 DRAWERS	1357+2018 x 700 x 850+100	01	RETAINED
06	S/S TWO LEVEL PASS SHELF ON GANTRY OVER PENINSULA	1800 x 350 x 800	02	RELOCATED
07	S/S CORNER BASE CABINET (CONFIRM DESCRIPTION)	2018+1200 x 700 x 850+100	01	RETAINED
08	S/S TWO LEVEL OVER SHELF	850 x 350 x 800	01	RETAINED
09	S/S TWO LEVEL OVER SHELF	1650 x 350 x 800	01	RESIZED
10	S/S LANDING TABLE BESIDE COOKING RANGE, UNDER SHELF	900 x 700 x 850	01	RESIZED
11	WORK TOP FREEZER - 180 — CHEF BASE OPPOSITE RANGE	1800 x 760 x 840	01	RELOCATED
12	WORK TOP CHILLER - 180 — CHEF BASE OPPOSITE RANGE	1800 x 760 x 840	01	RELOCATED
13	S/S BASE CABINET — MOVED FROM CORRIDOR TO DRY STORE	2337 x 500 x 850+100	02	RELOCATED
N2	S/S HAND WASH BASIN, KNEE / SENSOR OPERATED	400 x 400	01	NEW

KITCHEN CONSULTANT DESIGN REVIEW

Ground floor kitchen — assessment of the existing layout (A-01) and the proposed rearrangement (A-02)

INTENDED WORKFLOW — ONE-WAY, CLEAN TO DIRTY SEPARATED

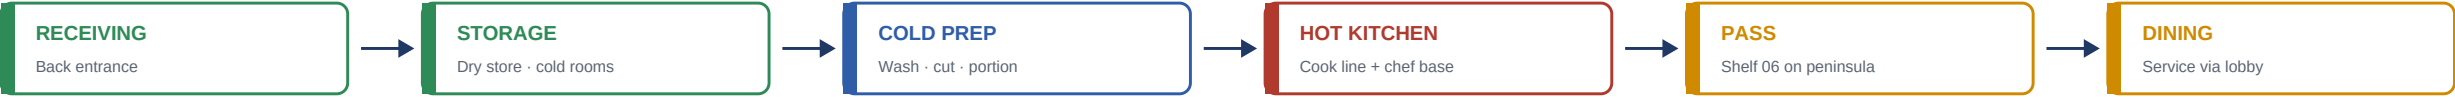

Dirty returns: dining → corridor → wash area (separate lane from goods-in; stagger delivery times with service).

FINDINGS ON THE EXISTING LAYOUT



#	AREA	FINDING	RISK	RESPONSE IN PROPOSED LAYOUT (A-02)
1	HOT KITCHEN	Centre island (chiller / wall cabinet / freezer) leaves side aisles of only 1000–1016 mm; the only route from the door to the cook line runs through them.	HIGH	Island removed. Refrigeration becomes a chef base on a peninsula; 1390 mm clear route from door to line.
2	HOT KITCHEN	Aisle between island and cook line is 1140 mm with oven doors opening into it.	MED	Chef base set at a 1200 mm cook aisle; cook turns 180° from range to W/T chiller / freezer.
3	COOK LINE	Trolley parked mid-line between oven and range; no landing space beside the range for pans or plates.	MED	Trolley moved to a trolley bay. Range moved 850 mm; 900 mm landing table (10) added.
4	HOT KITCHEN	No hand wash basin in the hot kitchen or cold prep.	HIGH	Hand wash basins N2 (hot kitchen) and N3 (cold prep entry) added.
5	COLD PREP	No sink for washing vegetables or thawing; raw produce must be carried to the wash area and back.	HIGH	Right return of C-shape counter replaced with a 1200 mm double bowl prep sink N1 on the outside wall.
6	CORRIDOR	Cabinets 13 (2 × 2337 × 500) cut the only circulation corridor to 800 mm; goods, service and dirty returns all share it.	HIGH	Cabinets moved to dry store; corridor clear width 1290 mm.
7	SERVICE	No defined pass: plated food is carried across the kitchen to the door.	MED	Pass shelf 06 on the peninsula, next to the door route; servers stay out of the cook aisle.
8	FABRICATION	Hot kitchen has ~11.6 m of prep counter plus over shelves; item 07 is described as an over shelf but sized as a base cabinet.	LOW	Hot prep counter cut to ~9.1 m + 0.9 m landing; two over shelves omitted. Confirm item 07.

BEFORE vs AFTER

MEASURE	EXISTING (A-01)	PROPOSED (A-02)
Cook aisle (range ↔ refrigeration)	1140 mm	1200 mm
Door → cook line route	1000 mm	1390 mm
Hot kitchen prep aisle	1000 / 1016 mm	1380 mm
Main corridor clear width	800 mm	1290 mm
Hand wash basins	0	2
Prep sink in cold prep	None	1 × double bowl
Landing beside range	None	900 mm
Hot kitchen S/S prep counter	~11.6 m	~9.1 m + landing

TO VERIFY ON SITE BEFORE FABRICATION

- ☐ Hood canopy covers the full cook line in its new order, with 150 mm overhang each end.
- ☐ Gas and power for the range moved ~850 mm left; oven power points stay close to where they are now.
- ☐ Floor boxes / power under the peninsula for the W/T chiller & freezer (2 × dedicated 13 A).
- ☐ Drainage & hot/cold water for prep sink N1 (outside wall) and hand wash basins N2, N3.
- ☐ Pass shelf gantry fixings on the peninsula; height 450 mm above worktop.
- ☐ Dry store wall can carry the relocated cabinets 13; check dry store door swing.
- ☐ Confirm item 07 (hot) description with the client before ordering.

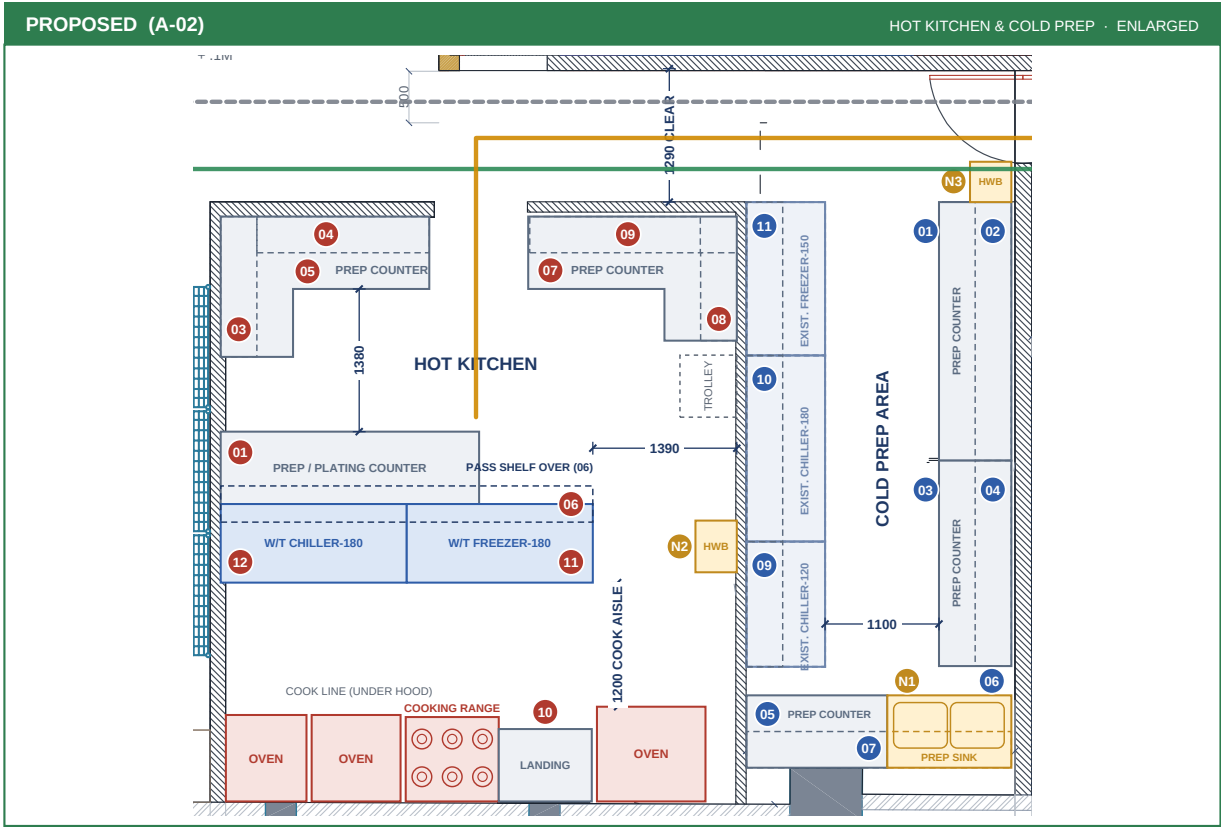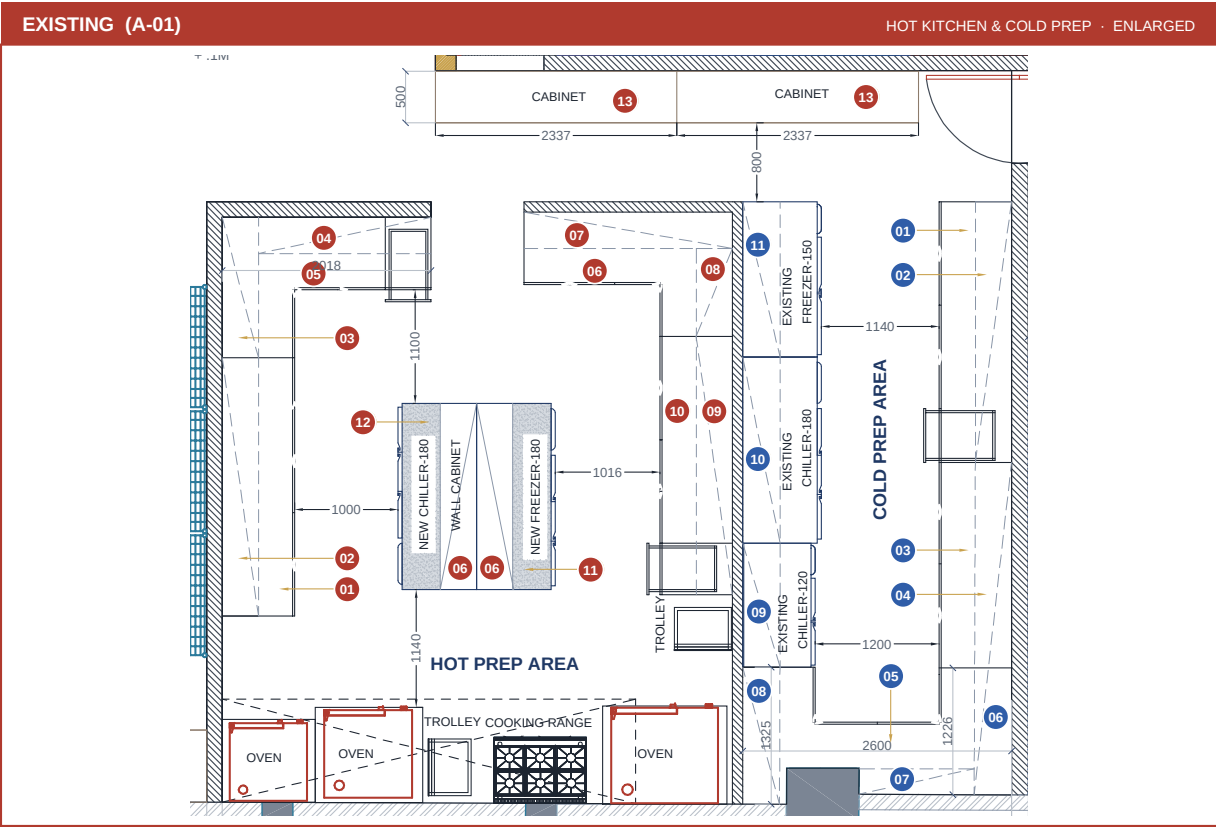

THE NEW DOHA KITCHEN
EQUIPMENT SERVICES W.L.L.

Commercial Kitchen & Cold Storage Solutions

P.O. Box 80247, Doha, Qatar | info@dkeqatar.com

PROJECT

RESTAURANT KITCHEN FIT-OUT

Ground Floor — Kitchen, Stores & Dining

DRAWING TITLE

DESIGN REVIEW
NOTES

Consultant findings & recommendations

FOR CLIENT REVIEW — NOT FOR FABRICATION

BASIS OF REVIEW

- Reviewed against drawing A-01 "Ground Floor Layout" dated 28.09.2026.
- Building shell, cold rooms, wash area, stair, dumbwaiter, dining and bar are unchanged.
- Cook line kept on the same wall so the existing hood, gas and exhaust routes can be reused.
- Existing refrigeration (freezer-150, chiller-180, chiller-120) kept in place.
- Clearances follow common commercial-kitchen practice: 1200 mm minimum where staff work back-to-back or pass hot equipment, 1000 mm minimum for a single working aisle.

FURTHER OPTIONS (NOT DRAWN)

- Heat lamps over pass shelf 06 if the menu is à la carte with plated hot dishes.
- Mobile ingredient bins under peninsula counter 01 for flour, rice and sugar at the point of use.
- Floor gully in front of the cook line for wash-down, falling away from the chef base.
- At a future refit, moving dishwasher nearer the dining door would take dirty returns off the goods-in route completely.

REVISIONS

R0	28.09.2026	Existing layout (A-01)
P1	29.09.2026	Proposed rearrangement
PREPARED BY TNDK DESIGN	CHECKED BY	
DATE 29.09.2026	SCALE NTS	
SHEET 02 OF 02	REVISION P1	

DRAWING NO.

TNDK-GF-A-03

P1